



HERRAMIENTAS DE VANGUARDIA, COSECHA 2025.

ENTRE LA OBRA NUEVA Y LA REHABILITACIÓN: UNA APROXIMACIÓN A LOS DETALLES CONSTRUCTIVOS EN ARQUITECTURA.

Profesoras:
Marlxi T. Pérez González y Elisa Bailliet Fernández.

Alumnos:
Lucas García Rivas; Erika Gómez Velasco; Daniela Losilla Serrano; María Isabel Olesiejuk Ayuso; Jorge Sánchez Escolar; Ana Tavira Melchor; Andrea Vargas Neciosup.

Acción financiada por la URJC en la convocatoria de Proyectos de Innovación Educativa 25/26 PIE25_10.



RESUMEN


El Proyecto de Innovación Educativa Herramientas de Vanguardia – Cosecha 2025 busca fortalecer la colaboración interdisciplinar del profesorado mediante el desarrollo de herramientas innovadoras que complementan la enseñanza tradicional y promueven metodologías activas centradas en la participación estudiantil. Desde esta concepción, el estudiantado se entiende como un "instrumento de vanguardia" capaz de generar, junto con el profesorado, análisis y recursos aplicados, configurando una "cosecha" conjunta derivada del contexto formativo desde 2024 en adelante.

El póster presentado recoge los resultados de la actividad Del detalle constructivo a la patología (V02), que integra investigación realizada sobre el parque inmobiliario del sur de Madrid con apoyo de los fondos Echegaray. El trabajo se desarrolla mediante un enfoque sistemático e interdisciplinar que fomenta una mirada crítica en el ámbito de la arquitectura.

En esta edición se dispuso de más tiempo lectivo, ya que el estudiantado había visitado la fábrica en cursos previos, lo que permitió profundizar en dos sistemas constructivos: la fachada de fábrica de ladrillo mediante el sistema GHAS y la rehabilitación con sistema SATE. Esta doble aproximación facilitó la comparación entre obra nueva e intervención en edificios existentes.


La herramienta V02 se articuló a través de la coordinación entre las asignaturas Sistemas Constructivos II y Patología, Edificación e Intervención. Primero, el estudiantado elaboró detalles constructivos de ambos sistemas; después se analizaron sus patologías asociadas, culminando con la exposición de resultados. Este intercambio de información evidencia la cohesión vertical entre cursos y consolidando un aprendizaje integrado y aplicado.

SISTEMA GHAS

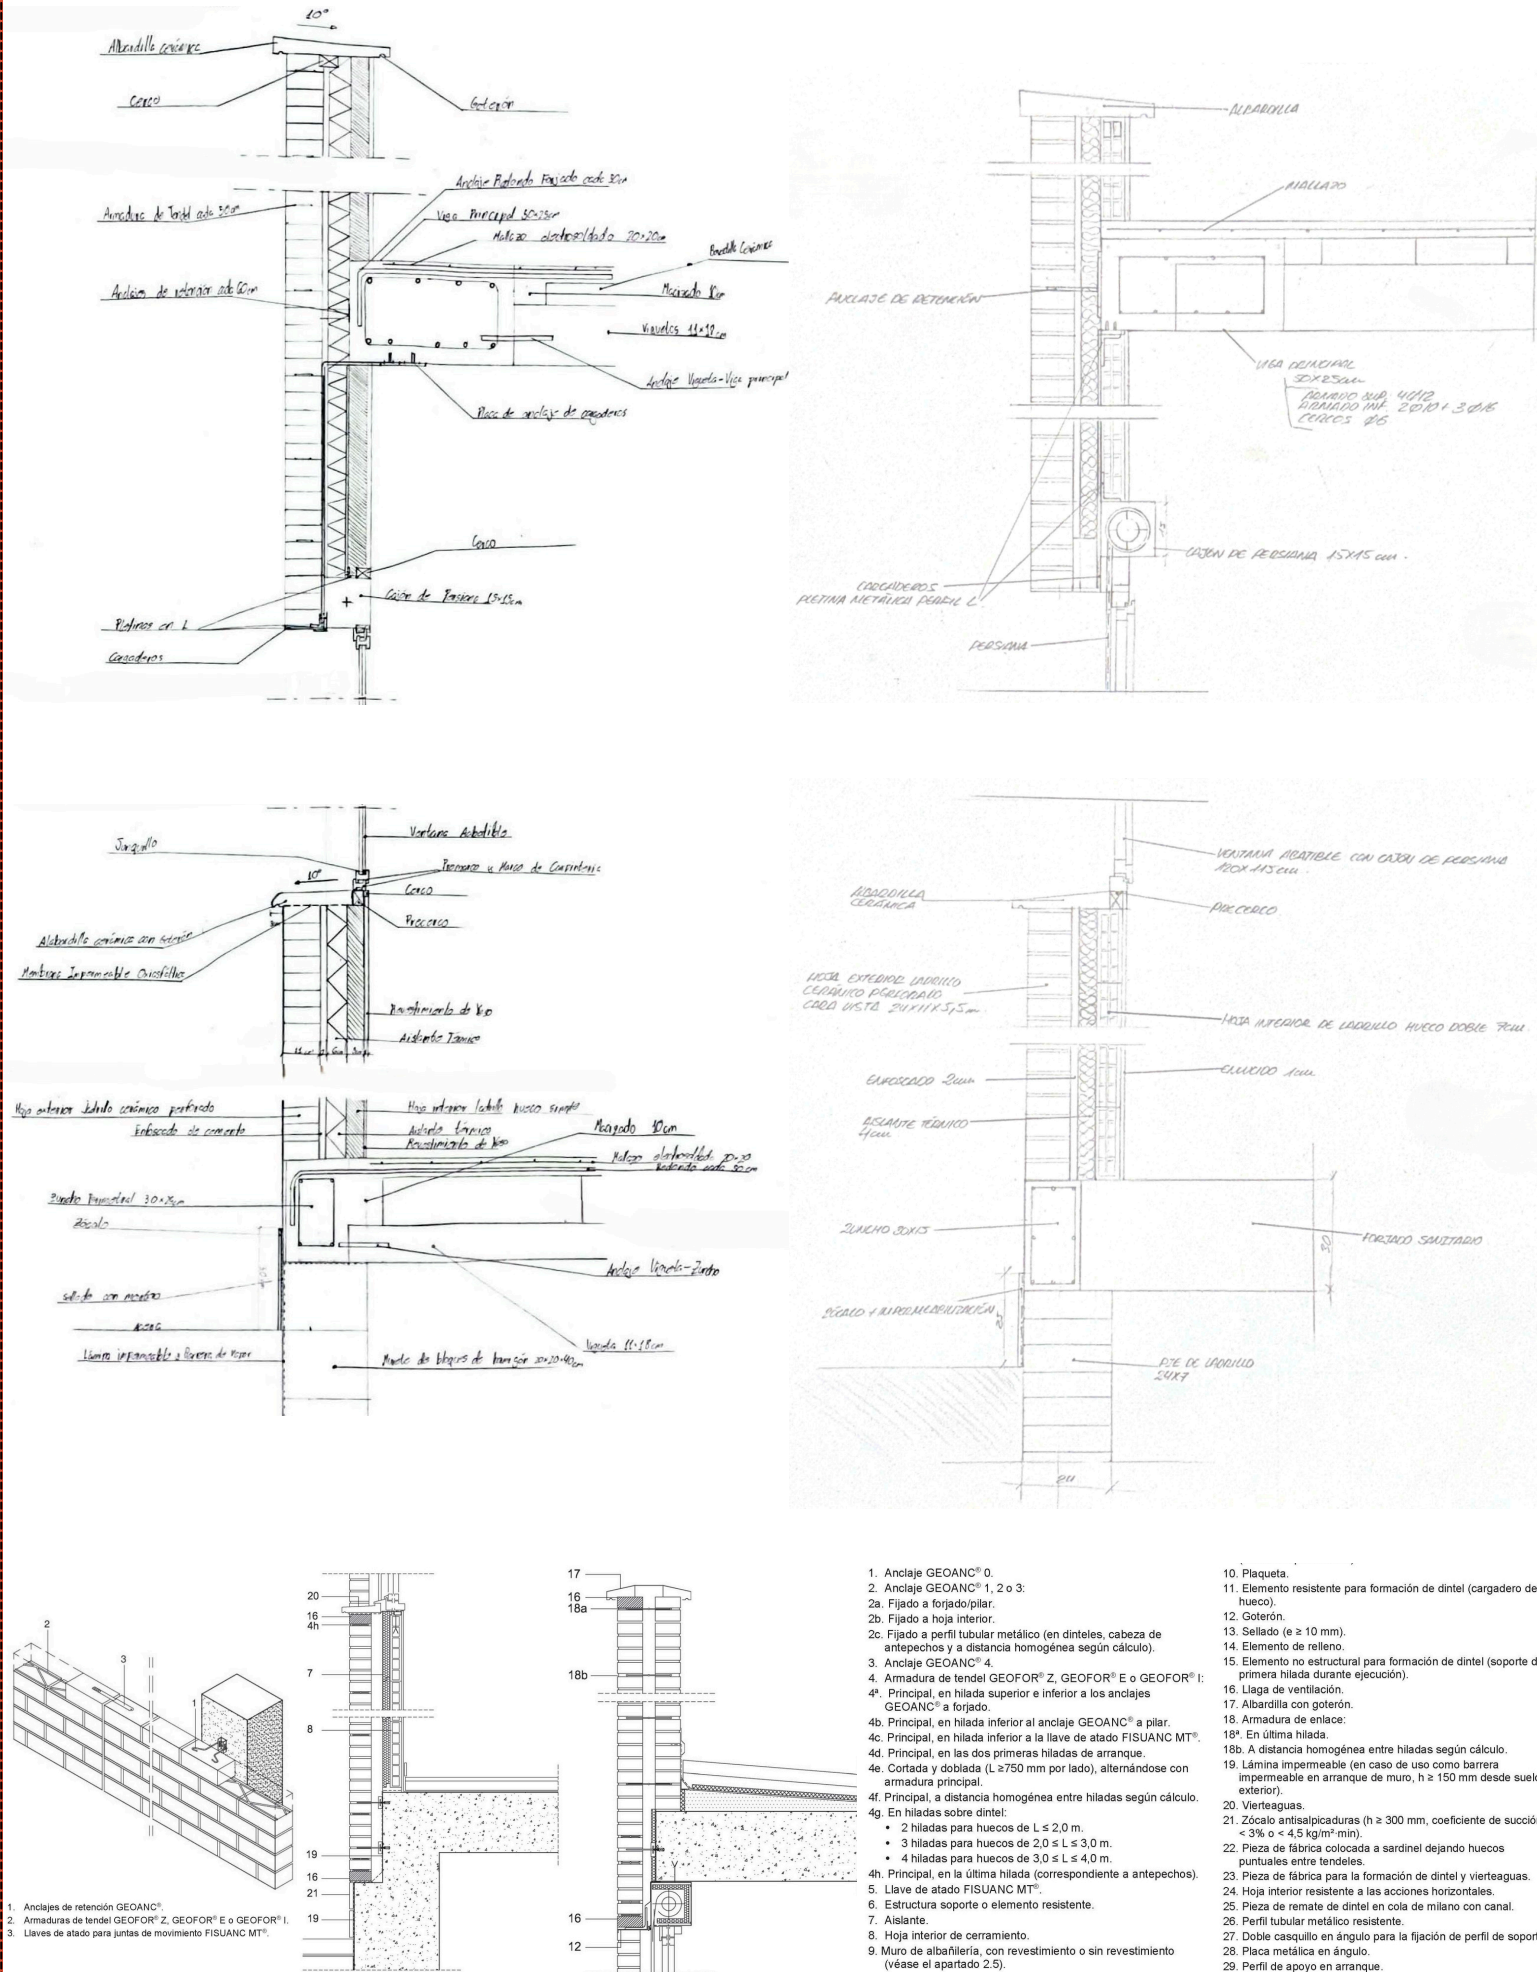

SISTEMA GHAS / Arranque sobre muro de cimentación / Peto con dos hojas trabadas / Fuente: <https://geohidrol.com>

REHABILITACIÓN CON SISTEMA SATE

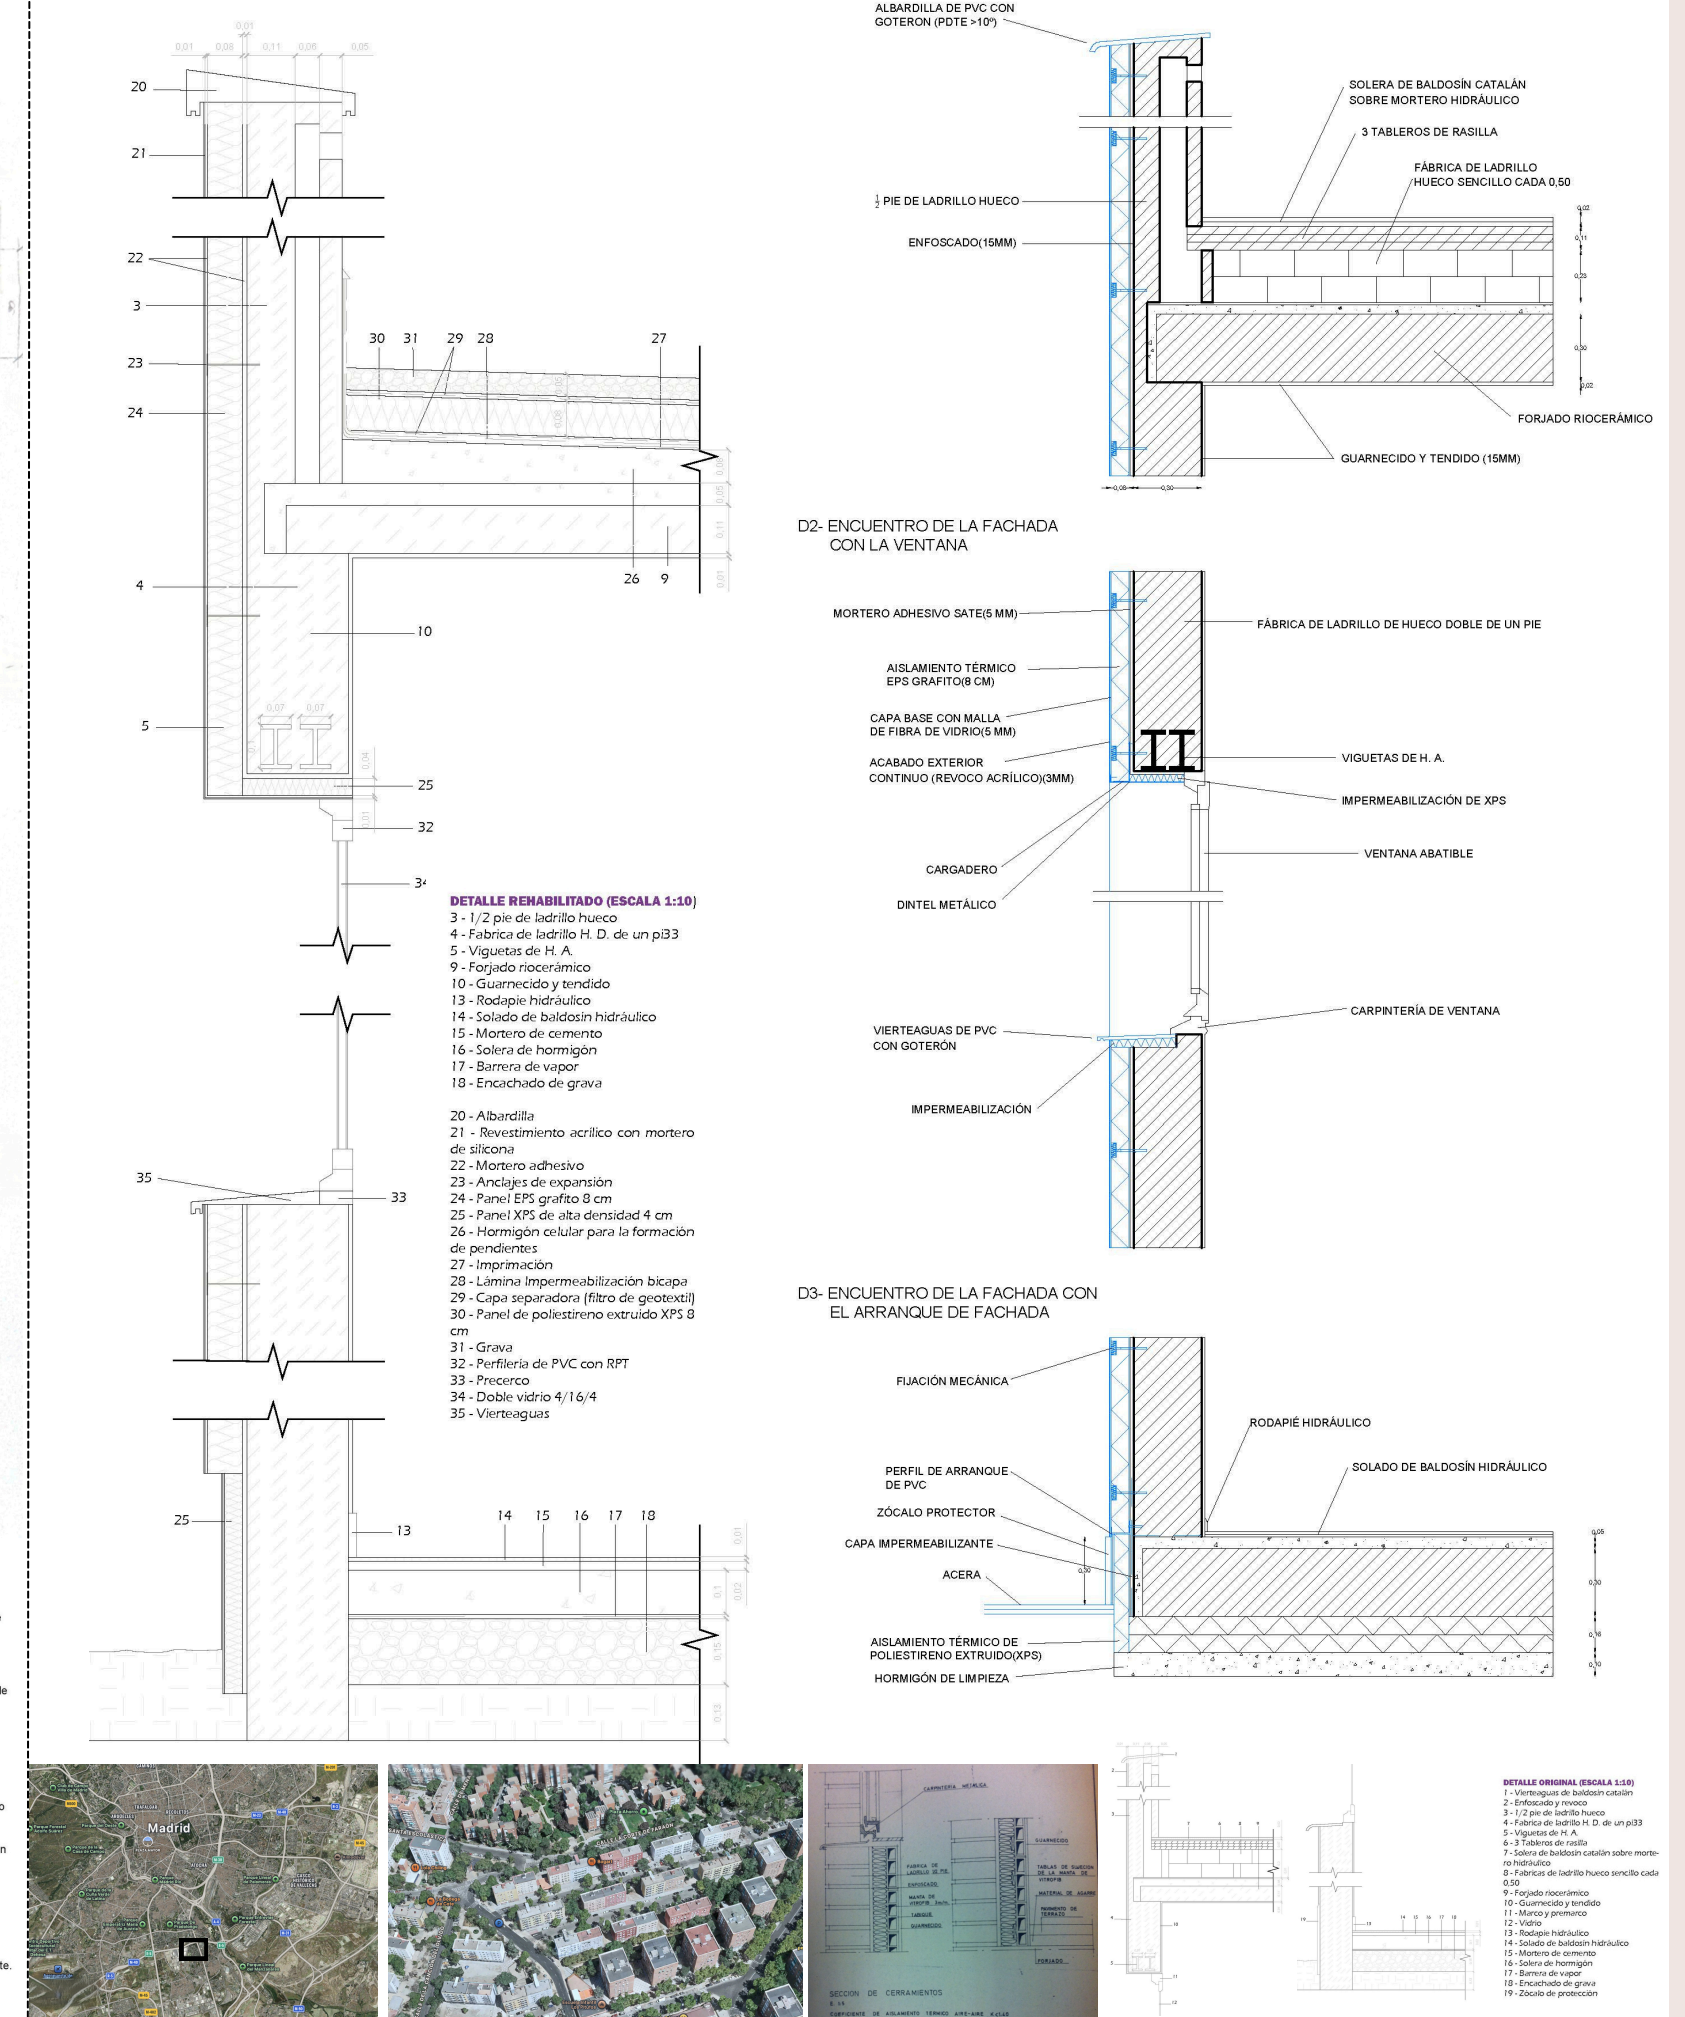

Madrid / Barrio Ciudad de los Ángeles - Tipología edificatoria / Fachada original

DEFINICIÓN DEL SISTEMA CONSTRUCTIVO

- SISTEMA CONSTRUCTIVO DE LOS FORJADOS
- SISTEMA CONSTRUCTIVO DE LA FACHADAS

DETALLES CONSTRUCTIVOS

- FACHADA TRADICIONAL
- FACHADA GHAS
- FACHADA VENTILADA

INSPECCIÓN VISUAL

- UN CASO DOCUMENTADO (BIBLIOGRAFÍA)
- UN CASO REAL DEL ENTORNO

IDENTIFICACIÓN Y REGISTRO DE PATOLOGÍAS

- FICHAS DE LESIONES

ELABORACIÓN DE UN INFORME

- DIAGNOSTICO
- PROPUESTA DE INTERVENCIÓN